


DO NOT SCALE | IF IN DOUBT, ASK

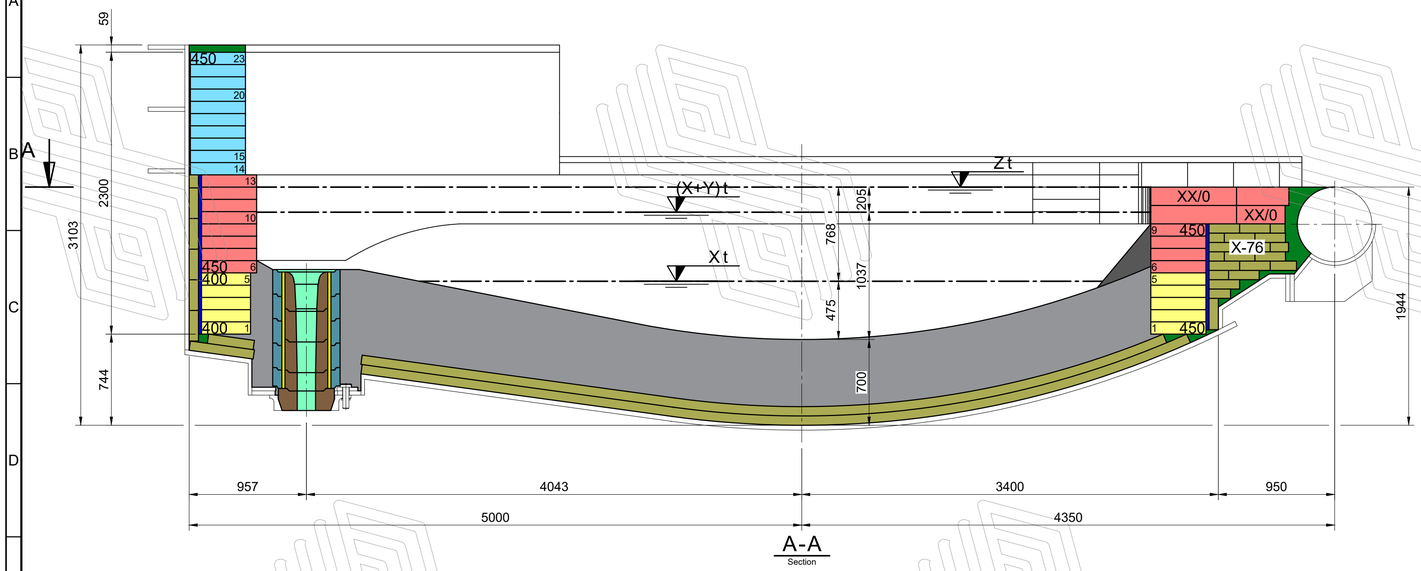

A-A
Section

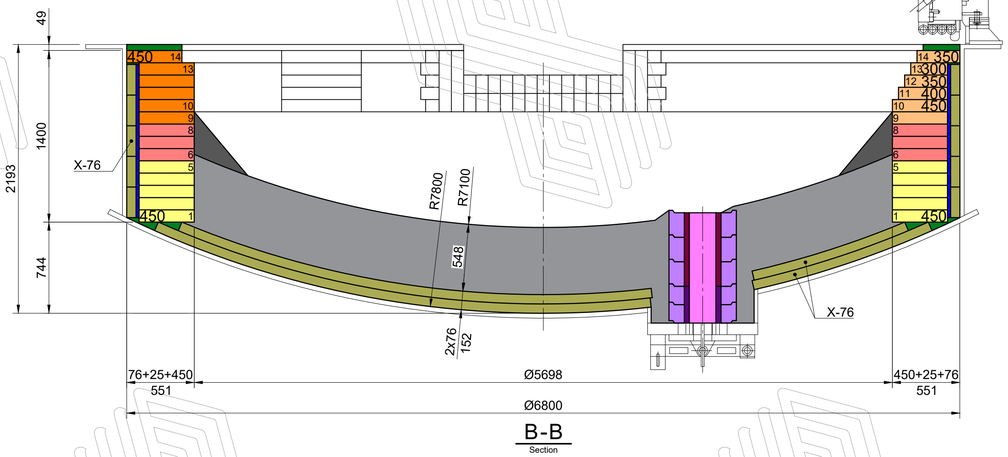



B-B
Section

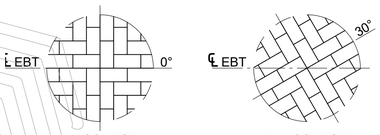


1st COURSE 2nd COURSE

PERMANENT LINNING ARRAGEMENT
Detail

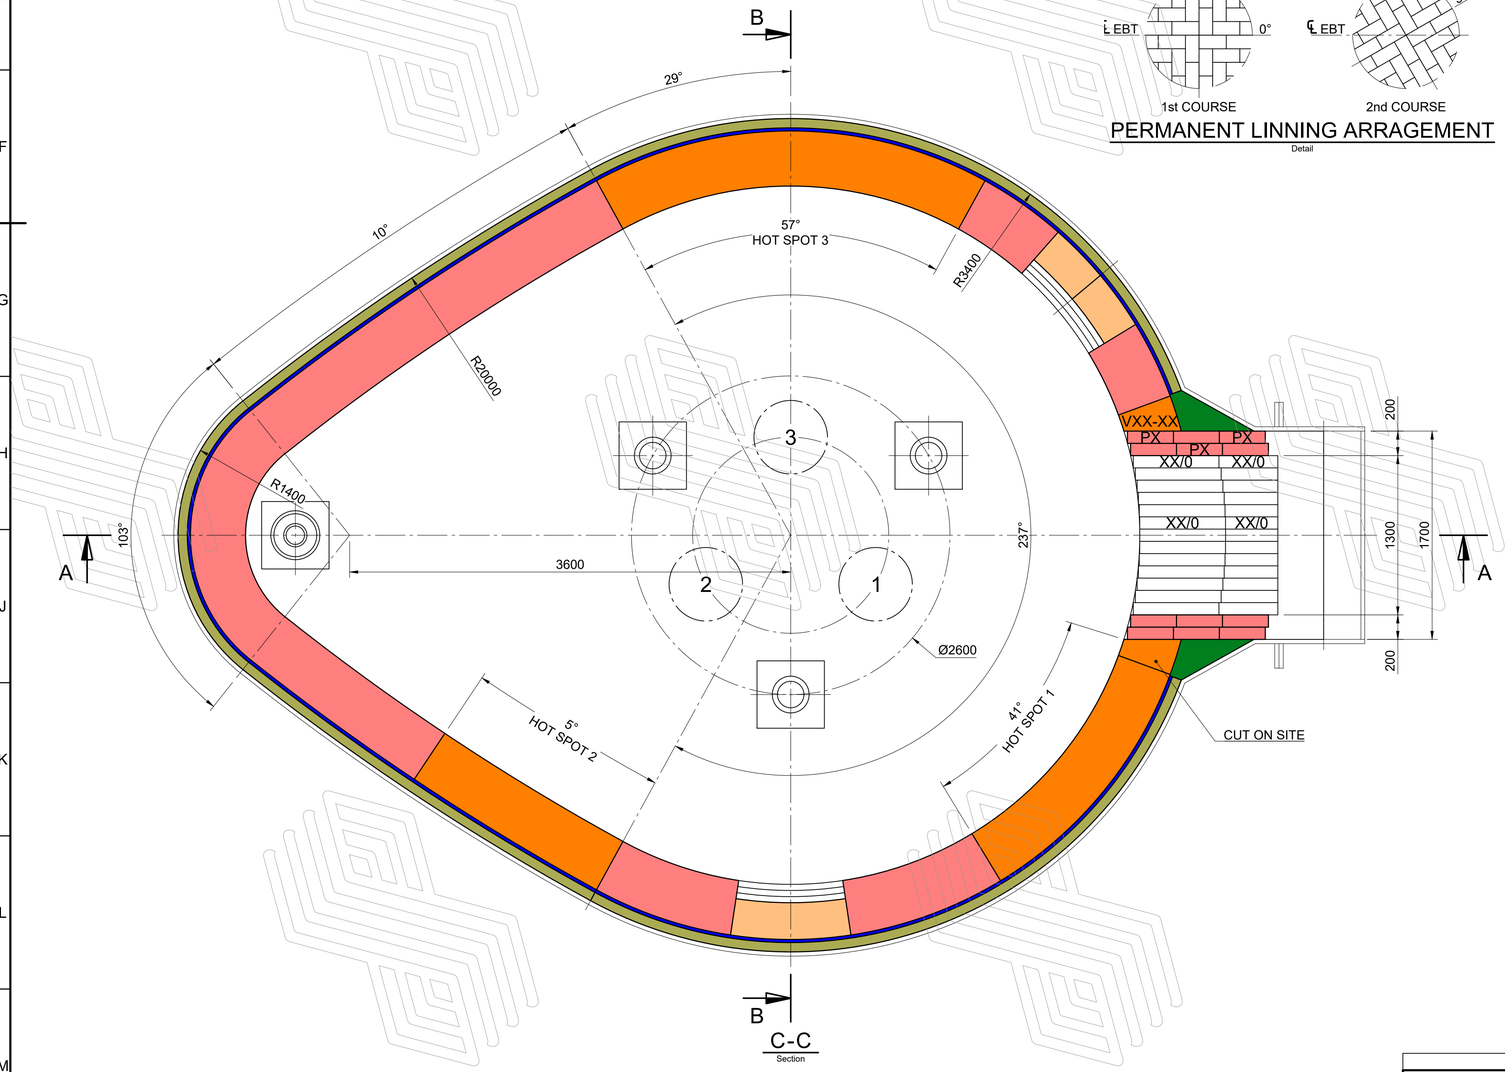

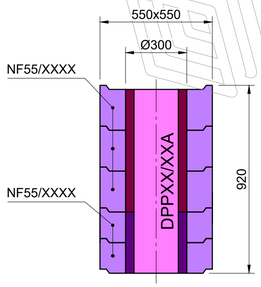

DPP SYSTEM
Detail
1:10

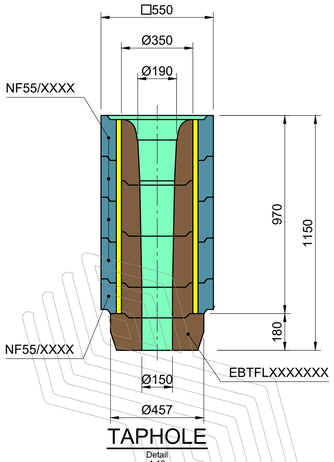

TAPHOLE
Detail
1:10

1. DIMENSIONS IN MILLIMETER.

	PERMANENT LINING	MORTAR
	WALL LOWER PART	
	SLAG ZONE	
	WALL UPPER PART	
	BURNER AREA	
	HOTSPOT	
	TAPHOLE SURROUNDING BRICKS	
	TAPHOLE SET	
	DPP SURROUNDING BRICKS	
	DPP PURGING PLUGS	
Brand		Mortar
	TAPHOLE ANNULAR GAP MIX	
	OLIVIA FILL	
	DPP RAMMING MIX - LP	
	DPP RAMMING MIX - UP	
	HEARTH	
	HEARTH BANKS	
	BACKFILLING MIX	
	RAMMING MIX	
Monolithic		Mixing liquid
	INSULATING FIBER	
Fiber material		Mortar / Glue

for approval

Company:

Approved ☐
Approved as corrected ☐
Revise and resubmit ☐
Rejected ☐

by:

Date:

Rev.	State	Date	Name (Drawn)	Date	Name (Checked)	Modification

We retain the copyright to these drawings and any accompanying enclosures. Such documents are provided to the addressee for personal use only. These documents may not be copied or reproduced without our written permission; it is also strictly prohibited to provide them or make them available to third parties, especially competitors. Illegal use by the addressee and or by third parties will result in civil and criminal legal action. The drawings and any enclosures must be returned to us if no order is placed.

Consignee

Client

Unit

Total order / offer

RHI MAGNESITA

	Date	Name	Scale
Drawn			1:25
Checked			

Former


Magnesita Refratários S.A.
Praça Louis Ensch 240
32210-902, Contagem-MG, Brazil

Size	Drawing number	Revision	State	Page	of
A1	CS	A00	R	01	02

		CS	BILL OF MATERIALS
Number	Document Type	Number	Document Type
Client documents		Additional Documents	

Document type: Lining drawing

DO NOT SCALE | IF IN DOUBT, ASK

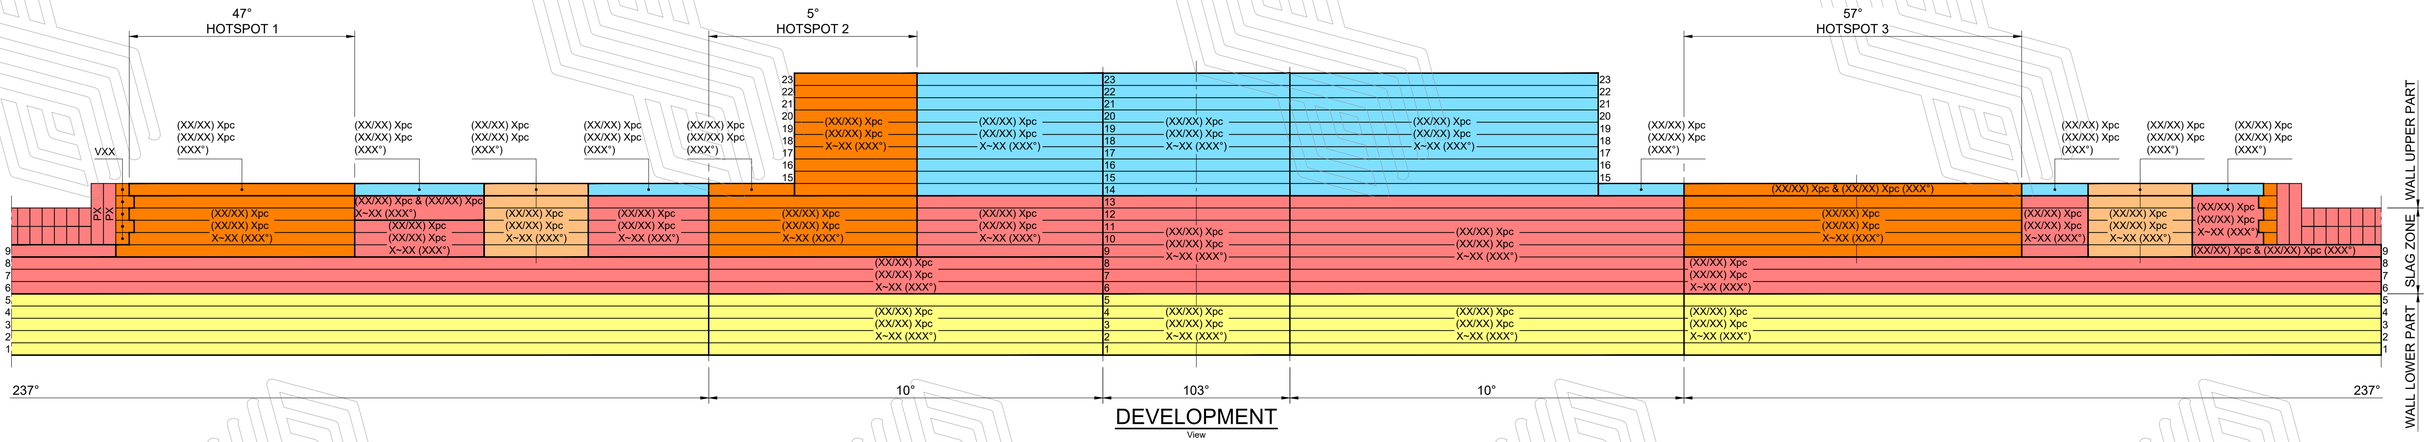

DEVELOPMENT

View

1. DIMENSIONS IN MILLIMETER.

	PERMANENT LINING	MORTAR
	WALL LOWER PART	
	SLAG ZONE	
	WALL UPPER PART	
	BURNER AREA	
	HOTSPOT	
	TAPHOLE SURROUNDING BRICKS	
	TAPHOLE SET	
	DPP SURROUNDING BRICKS	
	DPP PURGING PLUGS	
Brand		Mortar
	TAPHOLE ANNULAR GAP MIX	
	OLIVIA FILL	
	DPP RAMMING MIX - LP	
	DPP RAMMING MIX - UP	
	HEARTH	
	HEARTH BANKS	
	BACKFILLING MIX	
	RAMMING MIX	
Monolithic		Mixing liquid
	INSULATING FIBER	
Fiber material		Mortar / Glue

for approval

Company:

Approved ☐
Approved as corrected ☐
Revise and resubmit ☐
Rejected ☐

by:

Date:

Rev.	State	Date	Name (Drawn)	Date	Name (Checked)	Modification

We retain the copyright to these drawings and any accompanying enclosures. Such documents are provided to the addressee for personal use only. These documents may not be copied or reproduced without our written permission; it is also strictly prohibited to provide them or make them available to third parties, especially competitors. Illegal use by the addressee and or by third parties will result in civil and criminal legal action. The drawings and any enclosures must be returned to us if no order is placed.

Consignee

Client

Unit

Total order / offer

RHI MAGNESITA

	Date	Name
Drawn		
Checked		

Scale 1:25

Magnesita Refratários S.A.
Praça Louis Ensch 240
32210-902, Contagem-MG, Brazil

Former

Size	Drawing number	Revision	State	Page	of
A1	CS	A00	R	02	02

		CS	BILL OF MATERIALS
Number	Document Type	Number	Document Type
Client documents		Additional Documents	

Document type: Lining drawing